
שבלונת קידוח — תושבות Double-T ועיגון ארונות BESS

כל גדר — BESS + PV — ברקן — אורי פלסט, אזור תעשייה

E-20

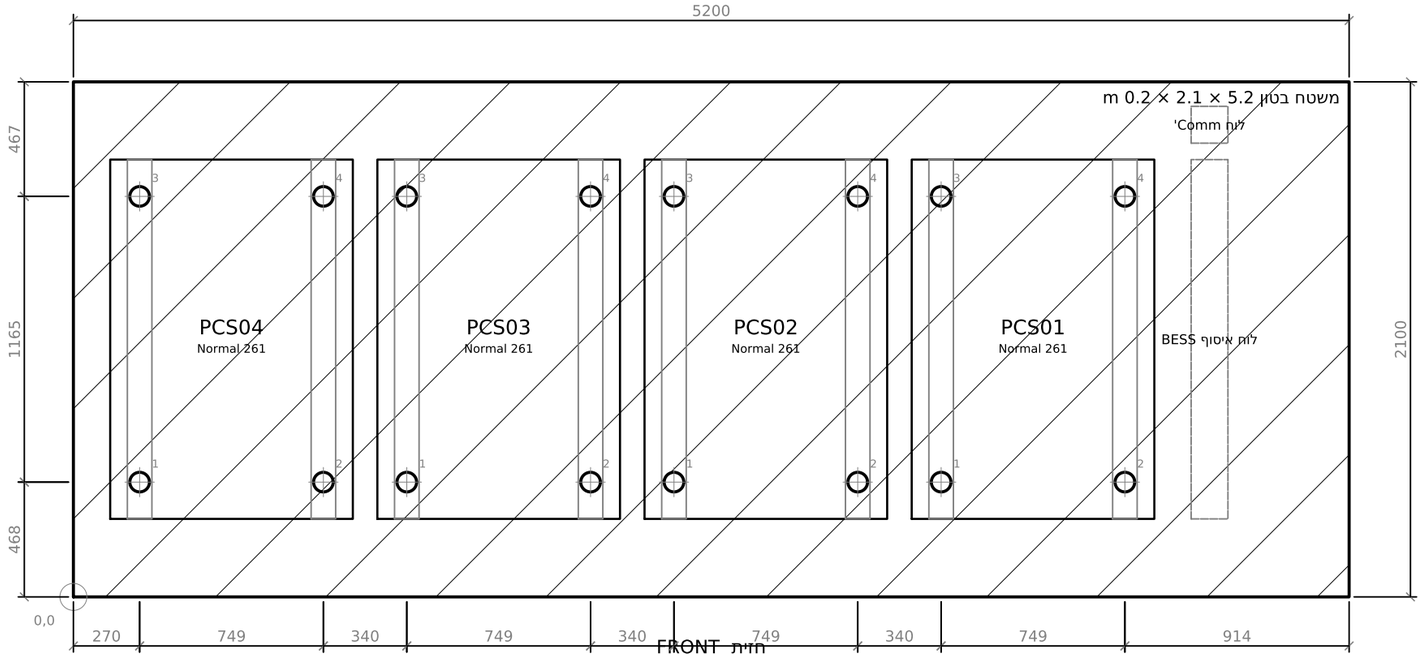

מבט על — שבלונת קידוח 1:25

קואורדינטות עוגנים מנקודת האפס

עוגן	X [mm]	Y [mm]
PCS04-1	270	468
PCS04-2	1019	468
PCS04-3	270	1633
PCS04-4	1019	1633
PCS03-1	1359	468
PCS03-2	2108	468
PCS03-3	1359	1633
PCS03-4	2108	1633
PCS02-1	2448	468
PCS02-2	3197	468
PCS02-3	2448	1633
PCS02-4	3197	1633
PCS01-1	3537	468
PCS01-2	4286	468
PCS01-3	3537	1633
PCS01-4	4286	1633

מפרט עיגון


סוג עוגן	עוגן כימי (אפוקסי/היברידי) + מוט הברגה מגולוון — לאימות
בורג	M16
קוטר קידוח	Ø18 מ"מ
עומק קידוח	125 מ"מ
מומנט הידוק	לפי יצרן
כמות	16 עוגנים (4 לארון × 4)
מרחק שפה מינ'	150 מ"מ
מרווח מינ'	150 מ"מ

הערות

1. מידות הארון (Roche Energy NORMAL C&I CABINET_261 (2026 — מדף הנתונים כ-2.7 טון, גובה 2471, 1465×989).
2. משטח הבטון 5.2×2.1×0.2 מ' — לפי פרט קונסטרוקטור; טבעת הארקת יסוד Ø10 ופלח 50×4 Fe לפי G006.
3. תבנית הקדיחה: 2 קורות T לכל ארון, 2 עוגנים לכל קורה (סה"כ 4 לארון). ממדי הקורה ומיקום החורים — לפי פרט הספק.
4. קידוח לאחר אשפרת הבטון; ניקוי החור באוויר דחוס ומברשת לפני הזרקת הדבק; מומנט הידוק לפי יצרן העוגן.
5. אין לקדוח בטווח 150 מ"מ מקצה המשטח; יש לאתר ברזל זיון לפני הקידוח (סורק).
6. כל הערכים בגיליון זה — טיוטה להדגמה; מחייב אישור מהנדס ובדיקה מול שרטוט הבסיס של יצרן הארון.
7. לאימות: שרטוט בסיס הארון (base frame) ומיקום חורי העיגון מיצרן הארון — הערכים כאן הם תבנית ברירת מחדל (120/150 מ"מ מהפינה).
8. לאימות: פרופיל קורות ה-Double-T, אורכן וגובהן (200?) — לפי ספק הקורות.
9. לאימות: סוג העוגן והעומק — לפי חישוב עומס (משקל 2.7 טון לארון, רוח/רעידת אדמה) ואישור קונסטרוקטור.

קורות Double-T — קורות פלדה T מגולוונות — לפי פרט ספק (Roche/Afcon), גובה 200 מ"מ

פרט ארון Normal 261 — תבנית קידוח 1:20

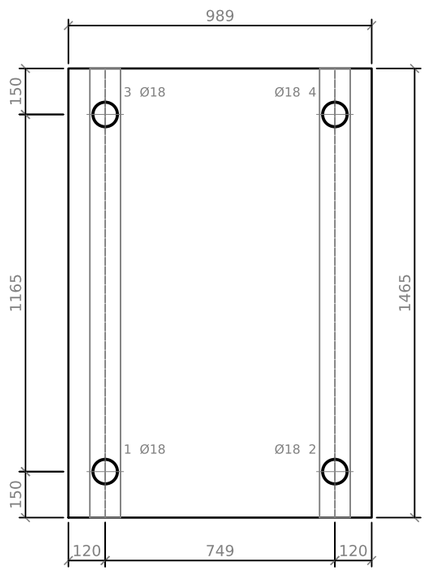

מהדורה	תאריך	מהות העדכון
A	2026-10-17	טיוטה ראשונה — תבנית קידוח, לאימות מול שרטוט בסיס היצרן

מתכנן: ברק הנדסת חשמל — מזמין: אפקון אגירה — לעיון

פרויקט: כל גדר — BESS + PV — ברקן — אורי פלסט, אזור תעשייה

שם התוכנית: שבלונת קידוח — תושבות Double-T ועיגון ארונות BESS

גיליון	קנ"מ	תאריך	מהדורה	מס' תוכנית
1/1	1:25 / 1:10	2026-10-17	A	E-20