אורי פלסט — BESS1 (18×261kWh)

ברקן — אורי פלסט, אזור תעשייה

מזמין: אפקון אגירה

מתכנן: ברק הנדסת חשמל

לעיון

מהדורה A · 2026-10-17

רשימת גיליונות

גיליון	שם הגיליון	קנ"מ	מהד'
E-00	דף שער — רשימת גיליונות ונתוני הפרויקט	-	A
E-20	שבלונת קידוח — תושבות Double-T ועיגון 18 ארונות BESS1	1:100 / 1:15	A

נתוני הפרויקט

לקוח	אפקון אגירה
אתר	ברקן — אורי פלסט, אזור תעשייה
סטטוס	לעיון
מהדורה / תאריך	A / 2026-10-17
לוחות מתח נמוך	0 (0 מעגלים)
מסדרי מתח גבוה	0 (0 תאים)
צמתים (ממיר/אגירה/PV)	-
ארונות BESS / משטח	18 × Normal 261 · 20.5×1.8 m
גליונות בסט	2

מהדורות

מהד'	תאריך	תיאור
A	2026-10-17	טיוטה לפי G003 BESS1 (Roche, 08.09.26): משטח 18, 20.5×1.8 ארונות ברווח 100, 500 מהקצה

פריטים פתוחים לאימות

המשטח (150 מהחזית?) ואורך 20.5 מ' — מול ה-DWG של G003 (בקובץ ה-PDF קיימים המספרים 240/210/300/120/150 שלא פוענחו).

1. מיקום השורה בעומק
2. שרטוט מסגרת הבסיס של REL261 (חורי החיבור לקורה) — לבקש מ-Roche Energy / אפקון אגירה.
3. פרופיל הקורה והעוגן — אישור קונסטרוקטור (144 עוגנים; עומס 18×2.8 טון).

סט זה הופק אוטומטית ממודל התכנון (bee-cad). כל ערך בגיליונות מקורו במודל או במקור המצוין בהערות; פריטים המסומנים "לאימות" אינם מאושרים לביצוע.

מהות העדכון	תאריך	מהד'
טיוטה לפי G003 BESS1 (Roche, 08.09.26): משטח 18, 20.5×1.8 ארונות ברווח 100, 500 מהקצה	2026-10-17	A

מתכנן: ברק הנדסת חשמל — מזמין: אפקון אגירה — לעיון

פרויקט: אורי פלסט — BESS1 (18×261kWh) — ברקן — אורי פלסט, אזור תעשייה

שם התוכנית: דף שער — רשימת גיליונות ונתוני הפרויקט

גיליון	קנ"מ	תאריך	מהדורה	מס' תוכנית
1/2	-	2026-10-17	A	E-00


שבלונת קידוח — תושבות Double-T ועיגון 18 ארונות BESS1

אורי פלסט — BESS1 (18×261kWh) — ברקן — אורי פלסט, אזור תעשייה

E-20

קורות ושורות ברגים לכל ארון (X,Y מנקודת האפס; ±30 מציר הקורה)

ארון	X קורה שמ'	X קורה ימ'	Y שורה קד'	Y שורה אח'
PCS18	500	1489	300/400	1365/1465
PCS17	1589	2578	500/600	1565/1665
PCS16	2678	3667	300/400	1365/1465
PCS15	3767	4756	500/600	1565/1665
PCS14	4856	5845	300/400	1365/1465
PCS13	5945	6934	500/600	1565/1665
PCS12	7034	8023	300/400	1365/1465
PCS11	8123	9112	500/600	1565/1665
PCS10	9212	10201	300/400	1365/1465
PCS09	10301	11290	500/600	1565/1665
PCS08	11390	12379	300/400	1365/1465
PCS07	12479	13468	500/600	1565/1665
PCS06	13568	14557	300/400	1365/1465
PCS05	14657	15646	500/600	1565/1665
PCS04	15746	16735	300/400	1365/1465
PCS03	16835	17824	500/600	1565/1665
PCS02	17924	18913	300/400	1365/1465
PCS01	19013	20002	500/600	1565/1665

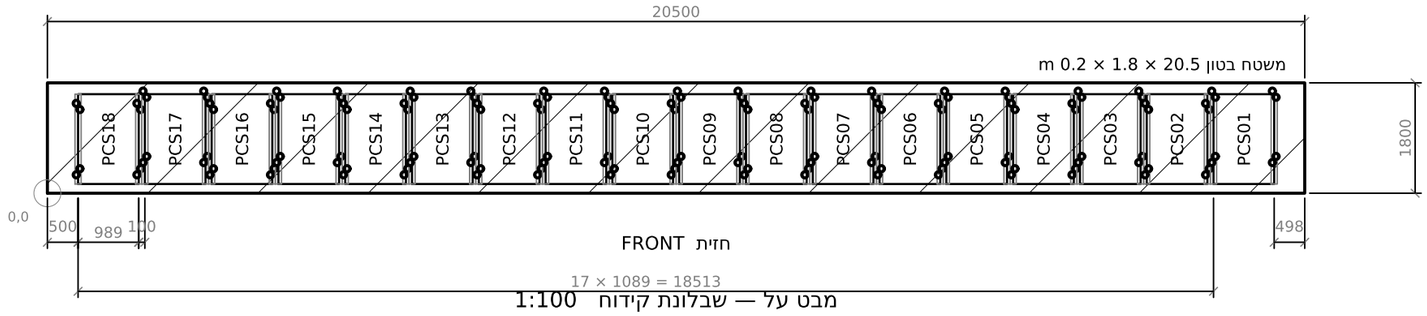


מבט על — שבלונת קידוח 1:100

מפרט עיגון

סוג עוגן	עוגן כימי Hilti HIT-HY 200-A + מוט HAS-U 8.8 מגולוון (או ש"ע) — לאימות
בורג	M16
קוטר קידוח	Ø18 מ"מ
עומק קידוח	125 מ"מ
מומנט הידוק	80 Nm
כמות	144 עוגנים (8 לארון × 18)
מרחק שפה מינ'	100 מ"מ
מרווח מינ'	100 מ"מ

קורות Double-T — IPE 200 מגולוון — "הגבהה קורות מתכת Double T" לפי G009, גובה 200 מ"מ

פרט ארון Normal 261 — תבנית קידוח 1:15

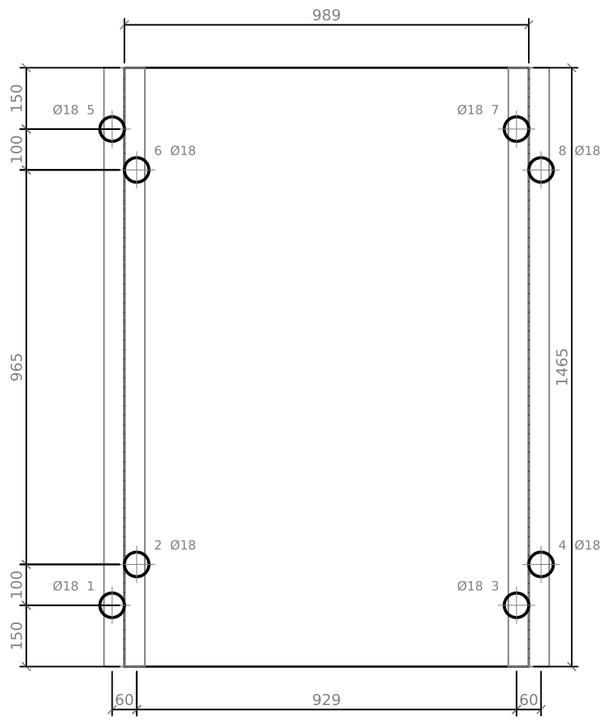

הערות

1. הארון: Roche Energy REL261 ("Normal 261" / Rochex by Afcon), גובה 2471, כ-2.8 טון (מדף נתונים Roche 2026). 1465×989 — 150 מקצה המשטח — הנחה, לאימות מול ה-DWG (ב-G003 סולם 400×100 על אבני שפה מאחורי השורה).
2. פריסה לפי RCH Uri Plast_BESS1 G003 (Roche/BorisH, 08.09.26): משטח 20.5×1.8×0.2 מ', 18 ארונות ברווח 100, 500 מהקצה השמאלי (קצה ימני 498); חזית הארון עיגון דרך האגף התחתון בזוג אלכסוני בכל קצה (±30 מהגוף, הסטה 100) — 4 לקורה, 8 לארון, 144 סה"כ.
3. ה-Double-T = פרופיל פלדה IPE 200 I, אגף 100) מתחת לכל קצה-צד של הארון לכל עומקו; עוגני קורות סמוכות ברווח ה-100 (נבדק אוטומטית); השורה האחורית המוסטת ב-135, Y=1665 מהקצה האחורי.
4. יחידות זוגיות מוסטות 200 מ"מ אחורה כדי לשמור ≥100 מ"מ בין ±30 מציר הקורה — בפרט 1:20. חיבור הארן לאגף העליון — לפי חורי מסגרת הבסיס של היצרן, קדיחה בשטח.
5. הטבלה: ציר כל קורה (X) ושורות הברגים (Y) לכל ארון; תבנית 2×; עוגן כימי M16 hef 125, מומנט 80 Nm; סבולת מיקום ±4 מ"מ; אין לקדוח בטווח 100 מ"מ מקצה המשטח.
6. קידוח לאחר אשפרת הבטון (≥7 ימים); איתור זיון בסורק; ניקוי החור ואורך 20.5 מ' — מול ה-DWG של G003 (בקובץ ה-PDF קיימים המספרים 240/210/300/120/150 שלא פוענחו).
7. לאימות: מיקום השורה בעומק המשטח (150 מהחזית?)
8. לאימות: שרטוט מסגרת הבסיס של REL261 (חורי החיבור לקורה) — לבקש מ-Roche Energy / אפקון אגירה.
9. לאימות: פרופיל הקורה והעוגן — אישור קונסטרוקטור (144 עוגנים; עומס 18×2.8 טון).

מהות העדכון	תאריך	מהד'
טיוטה לפי BESS1 (Roche, 08.09.26 G003): משטח 20.5×1.8, 18 ארונות ברווח 100, 500 מהקצה	2026-10-17	A

מתכנן: ברק הנדסת חשמל — מזמין: אפקון אגירה — לעיון

פרויקט: אורי פלסט — BESS1 (18×261kWh) — ברקן — אורי פלסט, אזור תעשייה

שם התוכנית: שבלונת קידוח — תושבות Double-T ועיגון 18 ארונות BESS1

גיליון	קנ"מ	תאריך	מהדורה	מס' תוכנית
2/2	1:100 / 1:15	2026-10-17	A	E-20