
חד-קווי מתח גבוה

מתחם אגירה — דוגמה 33kV — אתר לדוגמה, רמה ג

E-05

מסדר מ"ג — חדר פרטי — פס צבירה L1 L2 L3 630A 33kV 16kA/1s

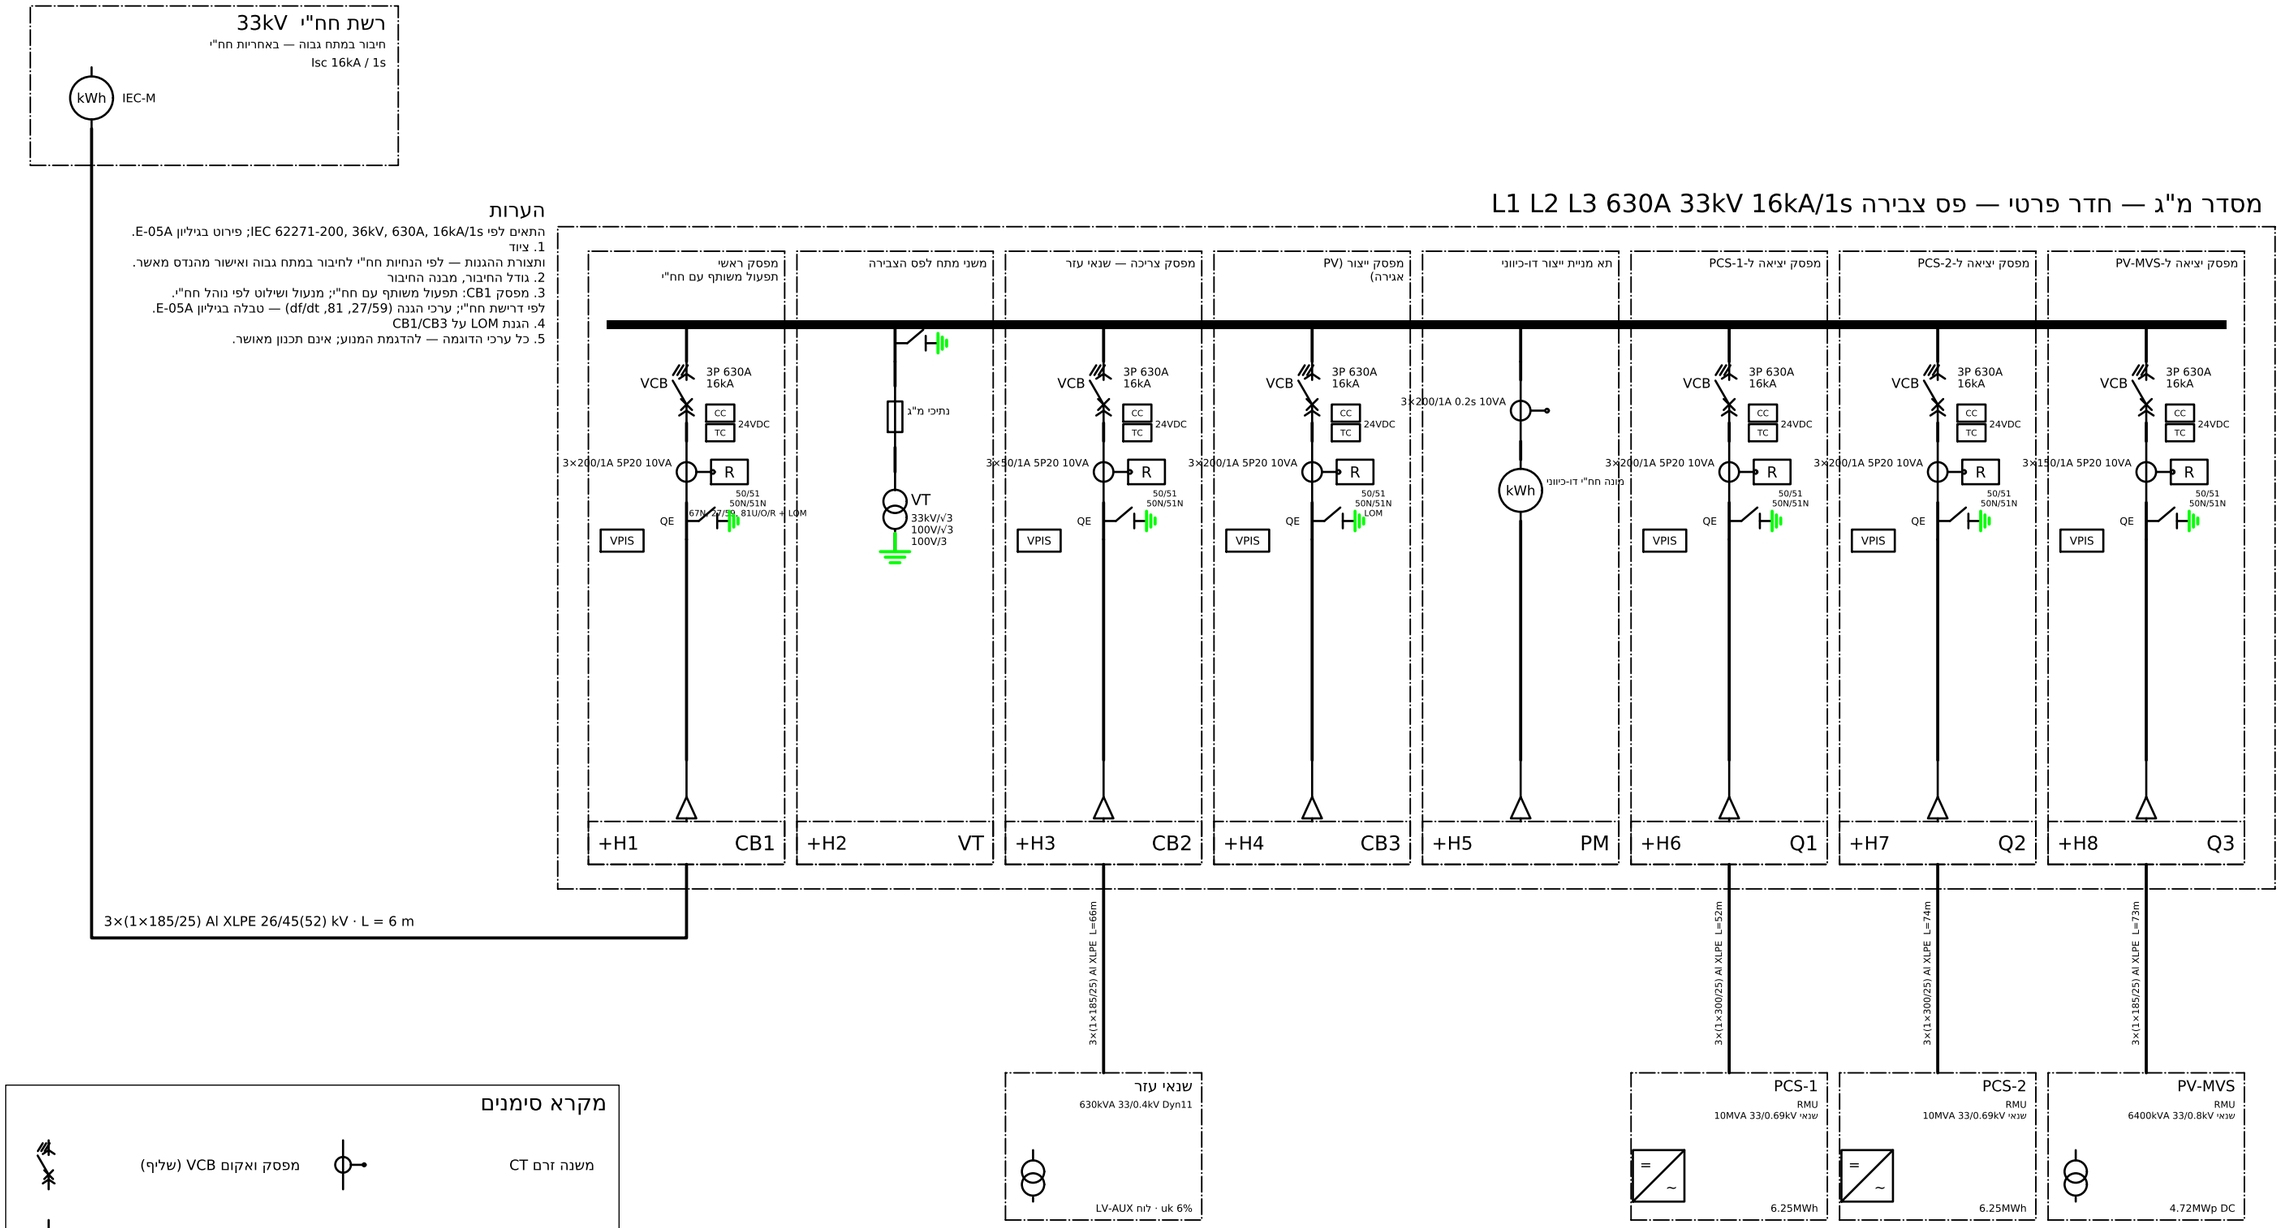

הערות

התאים לפי IEC 62271-200, 36kV, 630A, 16kA/1s; פירוט בגיליון E-05A.
1. ציוד
ותצורת ההגנות — לפי הנחיות חח"י לחיבור במתח גבוה ואישור מהנדס מאשר.
2. גודל החיבור, מבנה החיבור
3. מפסק CB1: תפעול משותף עם חח"י; מנעול ושילוט לפי נוהל חח"י.
לפי דרישת חח"י; ערכי הגנה (df/dt ,81 ,27/59) — טבלה בגיליון E-05A.
4. הגנת LOM על CB1/CB3
5. כל ערכי הדוגמה — להדגמת המנוע; אינם תכנון מאושר.

מקרא סימנים

- משנה זרם CT
- מפסק ואקום VCB (שליף)
- מנתק הארקה
- משנה מתח VT
- ראש כבל
- מחוון מתח VPIS
- מונה אנרגיה
- שנאי
- ממסר הגנה
- נתיך מ"ג

מהות העדכון	תאריך	מהד'
הגשה ראשונה — לעיון	2026-10-17	A

מתכנן: ברק הנדסת חשמל
מזמין: דוגמה — מנוע התכנון
לעיון

פרויקט: מתחם אגירה — דוגמה 33kV
אתר לדוגמה, רמה ג

שם התוכנית: חד-קווי מתח גבוה

גיליון	קנ"מ	תאריך	מהדורה	מס' תוכנית
1/2	ללא קנ"מ	2026-10-17	A	E-05

מפרט תאים וציוד — מסדר מ"ג — חדר פרטי

מסדר מ"ג — חדר פרטי — ציוד בכל תא

תא	תפקיד	מפסק	משני זרם	משני מתח / מנייה	הגנות	כבל יוצא / יעד
H1 CB1+	מפסק ראשי — תפעול משותף עם חח"י	3P 630A 16kA	3× 200/1A 5P20 10VA	—	50/51, 50N/51N, 67N, 27/59, 81U/O/R + LOM	3×(1×185/25) Al XLPE 26/45(52) kV · 6 m → רשת חח"י
H2 VT+	משני מתח לפס הצבירה	—	—	33kV/√3 / 100V/√3 / 100V/3	—	—
H3 CB2+	מפסק צריכה — שנאי עזר	3P 630A 16kA	3× 50/1A 5P20 10VA	—	50/51, 50N/51N	3×(1×185/25) Al XLPE · 66 m → שנאי עזר
H4 CB3+	מפסק ייצור (PV + אגירה)	3P 630A 16kA	3× 200/1A 5P20 10VA	—	50/51, 50N/51N + LOM	—
H5 PM+	תא מניית ייצור דו-כיווני	—	3× 200/1A 0.2s 10VA	33kV/√3 / 100V/√3 0.2	—	—
H6 Q1+	מפסק יציאה ל-PCS-1	3P 630A 16kA	3× 200/1A 5P20 10VA	—	50/51, 50N/51N	3×(1×300/25) Al XLPE · 52 m → PCS-1
H7 Q2+	מפסק יציאה ל-PCS-2	3P 630A 16kA	3× 200/1A 5P20 10VA	—	50/51, 50N/51N	3×(1×300/25) Al XLPE · 74 m → PCS-2
H8 Q3+	מפסק יציאה ל-PV-MVS	3P 630A 16kA	3× 150/1A 5P20 10VA	—	50/51, 50N/51N	3×(1×185/25) Al XLPE · 73 m → PV-MVS

ציוד משותף למסדר

1. פסי צבירה: L1 L2 L3 630A 33kV Icw 16kA/1s
2. מתח פיקוד: 24VDC
3. שלט אזהרה 'סכנת מתח גבוה', הארקת מסד, מהדקי כבלים — לפי IEC 62271-200 ונוהלי חח"י.

הערות

1. ציוד התאים לפי IEC 62271-200, 36kV, 630A, 16kA/1s; פירוט בגיליון E-05A.
2. גודל החיבור, מבנה החיבור ותצורת ההגנות — לפי הנחיות חח"י לחיבור במתח גבוה ואישור מהנדס מאשר.
3. מפסק CB1: תפעול משותף עם חח"י; מנעול ושילוט לפי נוהל חח"י.
4. הגנת LOM על CB1/CB3 לפי דרישת חח"י; ערכי הגנה (27/59, 81, df/dt) — טבלה בגיליון E-05A.
5. כל ערכי הדוגמה — להדגמת המנוע; אינם תכנון מאושר.

מהות העדכון	תאריך	מהד'
הגשה ראשונה — לעיון	2026-10-17	A

מתכנן: ברק הנדסת חשמל — מזמין: דוגמה — מנוע התכנון — לעיון

פרויקט: מתחם אגירה — דוגמה 33kV — אתר לדוגמה, רמה ג

שם התוכנית: מפרט תאים וציוד — מסדר מ"ג — חדר פרטי

גיליון	קנ"מ	תאריך	מהדורה	מס' תוכנית
2/2	ללא קנ"מ	2026-10-17	A	E-05A